
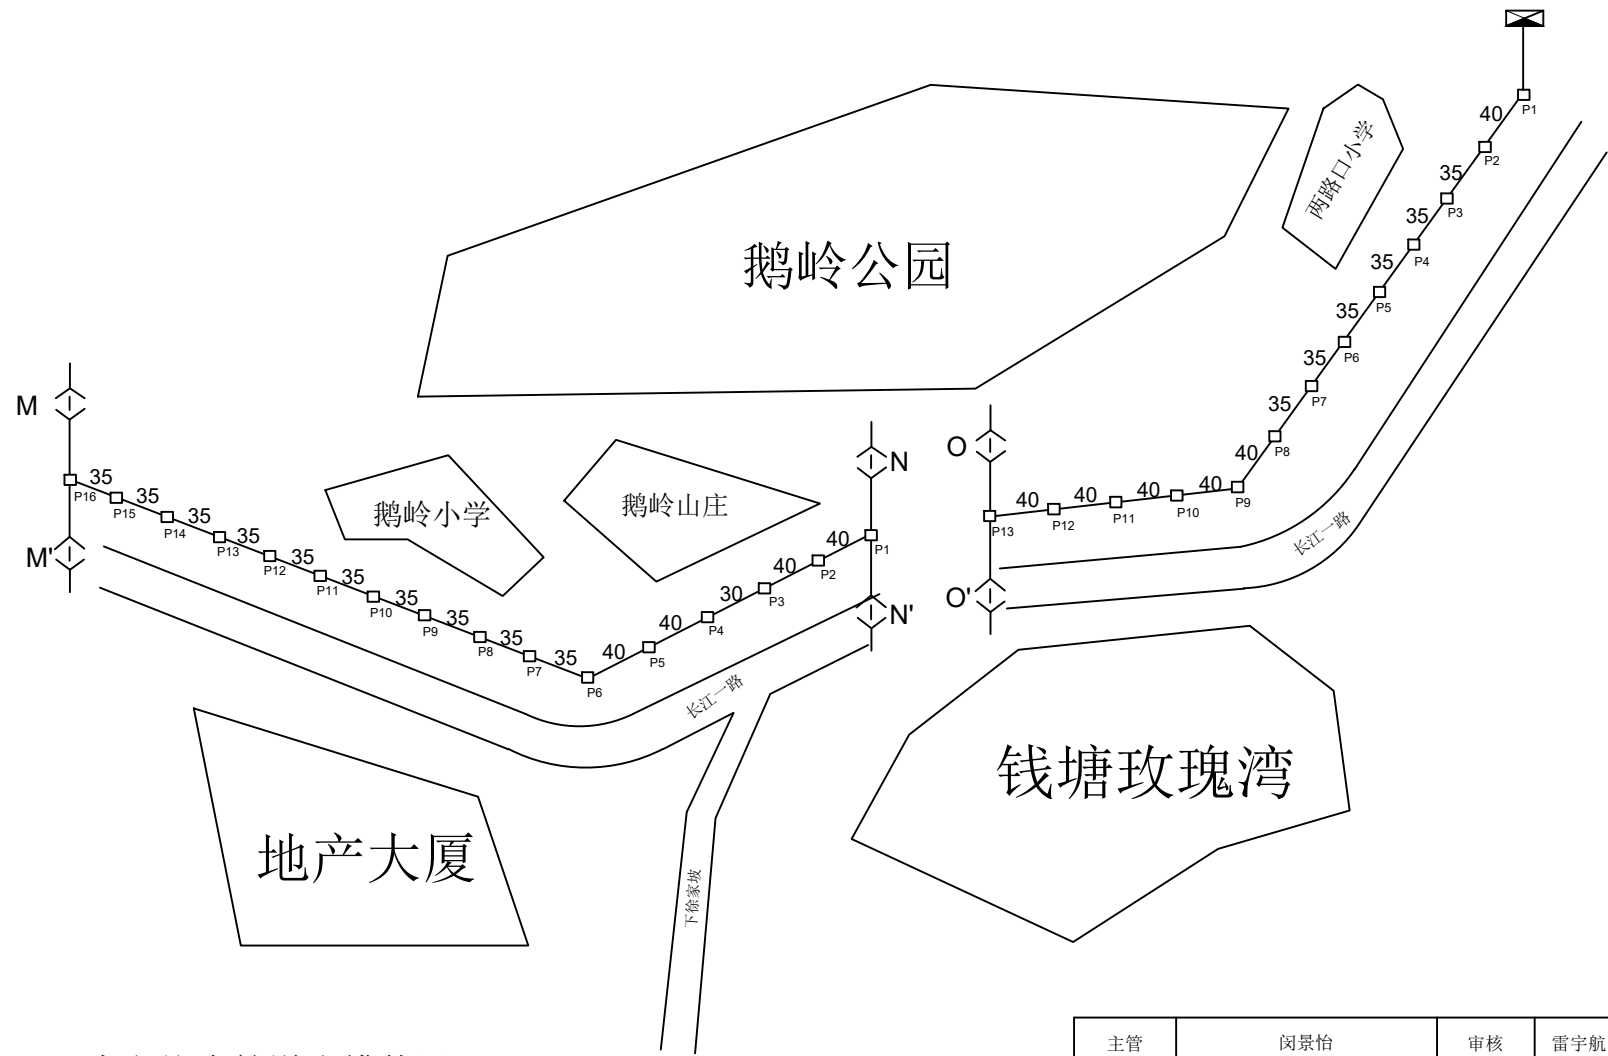


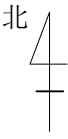

注：1. 本段均为管道光缆使用
GYTA53-48B1型号

主管	闵景怡	审核	雷宇航	第一组设计	
总负责人	闵景怡	制图/校核	闵景怡	接入机房平面布置及 走线架布局	
单项负责人	闵景怡	单位/比例	mm 1: 100		
设计	闵景怡	日期	2025/11/1	图号	5