

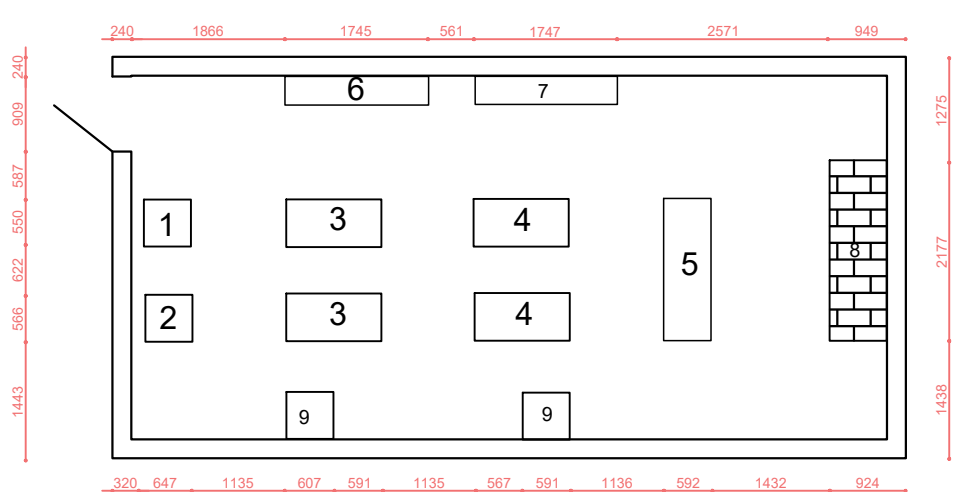


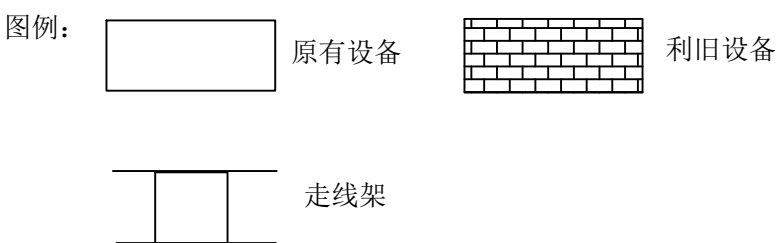

代号	设备名称	单位	数量
1	ODF架	架	1
2	SDH光端机	台	1
3	OTN光传输设备	台	2
4	蓄电池组	组	2
5	开关电源	套	1
6	BBU	台	1
7	SPN设备	台	1
8	综合柜	架	1
9	空调	台	2

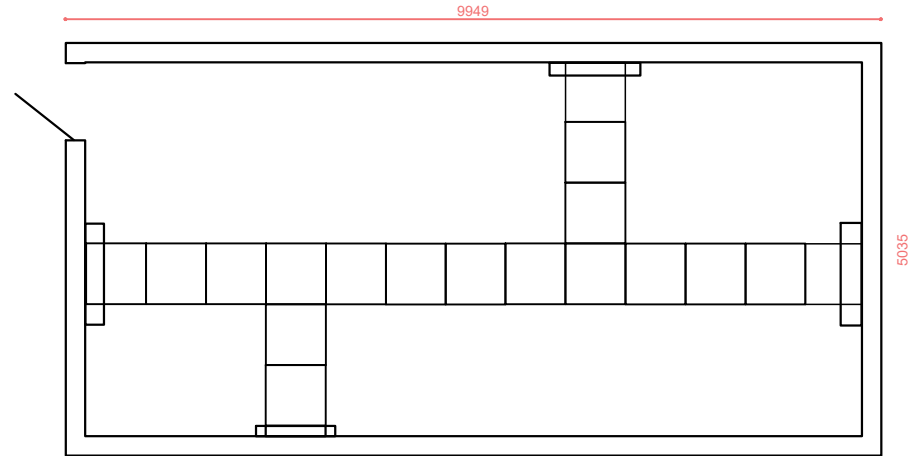

主管	邹佳辰	审核	雷宇航	第一组设计	
总负责人	邹佳辰	制图/校核	邹佳辰	接入机房平面布置及走线架布局	
单项负责人	邹佳辰	单位/比例	mm 1: 100		
设计	邹佳辰	日期	2025/11/5	图号	1